

ULTA BEAUTY WAREHOUSE

FRESNO, CALIFORNIA

PROJECT REPRESENTATIVES

OWNER:

REALTY INCOME TRUST 4
ATTN OM DPT#6066
11995 EL CAMINO REAL
SAN DIEGO, CA 92130
PHONE: 210-262-4278
CONTACT: DEREK ALLEN

CONSTRUCTION MANAGEMENT:

ALLEATO GROUP
8383 CRAIG STREET, SUITE 150
INDIANAPOLIS, IN 46250
PHONE: 727-599-4832
CONTACT: CANDON RUSIN

STRUCTURAL:

ALPER AUDI
6 CITYPLACE DRIVE, SUITE 1025
ST. LOUIS, MO 63141
PHONE: 314-432-8600
CONTACT: MICHAEL LUBIEWSKI

MECHANICAL:

ACCO ENGINEERED SYSTEMS
4980 E UNIVERSITY AVE #103
FRESNO, CA 9372
PHONE: 559-251-2226
CONTACT: KEITH DUNN

ELECTRICAL:

VALLEY UNIQUE ELECTRIC
75 PARK CREEK DR, SUITE 104
CLOVIS, CA 93611
PHONE: 559-237-4795
MARKW@VALLEYUNIQUE.COM

SHEET INDEX

MECHANICAL

M0.00	COVER SHEET, DRAWING INDEX, & SYMBOL LEGEND
M0.01	CONSTRUCTION REQUIREMENTS
M0.10	CONDITIONS OF APPROVAL
M1.01A	MECHANICAL LEVEL 01
M1.02	MECHANICAL ROOF
M5.01	DETAILS AND DIAGRAM
M10.01	ENERGY CODE
M10.02	ENERGY CODE (CONTINUED)

STRUCTURAL

S0.00	STRUCTURAL COVER SHEET
S0.01	GENERAL NOTES
S1.00	TYPICAL JOIST REINFORCEMENT
S2.00	EXISTING ROOF REINFORCING PLAN

ELECTRICAL

E-101	LEGEND AND NOTES
E-102	SINGLE LINE DIAGRAM
E-103	MECHANICAL EQUIPMENT SCHEDULE
E-104	PANEL SCHEDULE
E-105	FLOOR POWER PLAN
E-106	LEVEL 01 POWER PLAN
E-107	ROOF POWER PLAN
E-108	ELECTRICAL DETAILS
E-109	ENERGY CODE

DEFERRED SUBMITTALS

FIRE SPRINKLER MODIFICATIONS WILL BE SUBMITTED BY C-16 CONTRACTOR UNDER SEPARATE PERMITS

FIRE ALARM MODIFICATIONS WILL BE SUBMITTED UNDER A SEPARATE FIRE ALARM PERMIT WITH FRESNO FIRE DEPARTMENT

CODE ANALYSIS

GOVERNING CODE :

2022 CALIFORNIA BUILDING CODE
2022 CALIFORNIA PLUMBING CODE
2022 CALIFORNIA MECHANICAL CODE
2022 CALIFORNIA ELECTRICAL CODE
2022 CALIFORNIA FIRE CODE
2022 CALIFORNIA ENERGY CODE
2022 CALIFORNIA GREEN BUILDING STANDARDS

CODE ANALYSIS :

CONCRETE TILT-UP BUILDING

BUILDING OCCUPANCY:	MAIN S-1
OCCUPANCY SEPARATION:	ANCILLARY : B/A-3/H-3
CONSTRUCTION TYPE:	II-B
NUMBER OF STORIES:	1
BLDG. HEIGHT ALLOWED PER CBC 503	55'
AUTOMATIC FIRE SPRINKLER	YES
ALLOWABLE HEIGHT (W/ AUTOMATIC SPRINKLER)	75' (CBC 504.3)
ACTUAL PARAPET	42' TO 45'
ACTUAL AREA:	670,680 SF
ACTUAL AREA (BASIC)	S-1 = 17,500 SF
	B = 23,000 SF
ACTUAL AREA INCREASED ALLOWABLE	UNLIMITED PER CBC 507.4 SURROUNDED BY 60' CLEARANCE.
EXTERIOR WALL RATINGS:	NONE
EXTERIOR OPENINGS:	NONE
SEPARATION REQUIREMENTS:	NONE
OCCUPANT LOAD:	
OFFICE (28,089 SF @ 100 SF)	280
WAREHOUSE (642,591 SF @ 500 SF)	1,285
TOTAL OCCUPANT LOAD	1,565

AREA JUSTIFICATION :

SECTION 507

UNLIMITED AREA BUILDINGS

507.4 SPRINKLERED, ONE STORY
THE AREA OF A GROUP B, F, M OR S BUILDING NO MORE THAN ONE STORY ABOVE GRADE PLANE OF ANY CONSTRUCTION TYPE, SHALL NOT BE LIMITED WHERE THE BUILDING IS PROVIDED WITH AN AUTOMATIC SPRINKLER SYSTEM THROUGHOUT IN ACCORDANCE WITH SECTION 903.3.1.1 AND IS SURROUNDED AND ADJOINED BY PUBLIC WAYS OR YARDS NOT LESS THAN 60 FEET IN WIDTH

CBC 508.2 ACCESSORY OCCUPANCIES
ACCESSORY OCCUPANCIES ARE THOSE OCCUPANCIES THAT ARE ANCILLARY TO THE MAIN OCCUPANCY OF THE BUILDING OR PORTION THEREOF. ACCESSORY OCCUPANCIES SHALL COMPLY WITH THE PROVISIONS OF SECTIONS 508.2.1 THROUGH 508.2.4

A-3 TYPE OCCUPANCY (ALLOWABLE)
HEIGHT = 55' AREA = 9,500 S.F. PER CBC TABLE 504.3

B TYPE OCCUPANCY (ALLOWABLE)
HEIGHT = 55' AREA = 23,000 S.F. PER CBC TABLE 504.3

H-3 TYPE OCCUPANCY (ALLOWABLE)
HEIGHT = 55' AREA = 14,000 S.F. PER CBC TABLE 504.3

TENANT IMPROVEMENT
A-3 TOTAL AREA = 7,410 S.F.
B TOTAL AREA = 20,671 S.F.
H-3 TOTAL AREA = 16,565 S.F.
S-1 TOTAL AREA = 626,026 S.F.

CBC 508.2.1
(A-3 + B + H-3) 44,654 S.F. < 10% WHICH IS 67,068 S.F.
COMPLIES WITH CODE

CBC 508.2.3
A-3 < 9,500 S.F. PER CBC TABLE 508.2
B < 23,000 S.F. PER CBC TABLE 508.2
H-3 > 14,000 S.F. PER CBC TABLE 508.2

PER CBC 508.2.4 NO SEPARATION IS REQUIRED BETWEEN ACCESSORY OCCUPANCIES AND THE MAIN OCCUPANCY.

*H-3 OCCUPANCY ALLOWABLE DEFINED ON HARRINGTON REPORT.

PROJECT SCOPE :

COMMERCIAL ALTERATION/TENANT IMPROVEMENT TO INSTALL NEW RTUs, DESTRAIFICATION FANS, AND ASSOCIATED STRUCTURAL REINFORCING AND ELECTRICAL IN EXISTING WAREHOUSE (S-1), WITH NO WORK PROPOSED IN OFFICE OR ANCILLARY AREAS (B, A-3, H-3)

USE OF BUILDING :

EXISTING DISTRIBUTION WAREHOUSE (S-1) WITH ACCESSORY OFFICE (B), ASSEMBLY (A-3), AND HAZARDOUS (H-3) AREAS; NO WORK PROPOSED IN ACCESSORY/HAZARDOUS AREAS

PROJECT DATA & CODE SUMMARY

BUILDING & PLANNING DEPT. :

PLAN CHECK NO.:

OWNER/APPLICANT :

REALTY INCOME TRUST 4
ATTN OM DPT#6066
11995 EL CAMINO REAL
SAN DIEGO, CA 92130
PHONE: 210-262-4278
CONTACT: DEREK ALLEN

APPLICANT'S REPRESENTATIVE :

ALLEATO GROUP
8383 CRAIG STREET, SUITE 150
INDIANAPOLIS, IN 46250
PHONE: 727-599-4832
CONTACT: CANDON RUSIN

LEGAL DESCRIPTION :

REAL PROPERTY IN THE UNINCORPORATED AREA OF THE COUNTY OF FRESNO, STATE OF CALIFORNIA, DESCRIBED AS FOLLOWS:

PARCEL 2*

LOT 6 AND 7 OF CENTRAL CALIFORNIA COLONY COUNTY OF FRESNO, STATE OF CALIFORNIA, AS SHOWN ON MAP FILED BOOK 2, PAGE 1 OF MAPS, IN THE OFFICE OF THE COUNTY RECORDER SAID COUNTY.

APN: 329-130-02

PARCEL 3:

LOT 8 OF CENTRAL CALIFORNIA COLONY, ACCORDING TO THE MAP OR PLAT THEREOF ON FILE OR RECORD IN THE OFFICE OF THE COUNTY RECORDER OF THE COUNTY OF FRESNO, STATE OF CALIFORNIA, AND BEING IN THE SOUTHEAST QUARTER OF SECTION 27, TOWNSHIP 14 SOUTH, RANGE 20 EAST, MOUNT DIABLO BASE AND MERIDIAN EXCEPTING THEREFROM THAT PORTION DEEDED TO THE COUNTY OF FRESNO IN GRANT DEED RECORDED FEBRUARY 9, 1973 AS DOCUMENT NO. 13527, IN BOOK 6125 PAGE 960, OF OFFICIAL RECORDS.

APN: 329-130-11

ASSESSOR'S PARCEL NO. :

329-130-02, 329-130-11

ZONING :

GENERAL PLAN DESIGNATION: IL
INDUSTRIAL LIGHT

PROJECT DATA :

SITE AREA

In s.f.
In acres

BUILDING AREA

Main office
Hazardous Material (H-3)
Warehouse

Office: 1/300 s.f.
Warehouse: 1st 10k @ 1/2,000 s.f.
over 10k @ 1/5,000 s.f

TOTAL

Standard (9' x 19')
Van Pool/EV (9' x 19')
Accessible Stall (9' x 18')
Accessible Stall Van (12' x 18')

TOTAL

Trailer (10' x 55')

Zoning Designation - Industrial Light

MAXIMUM BUILDING HEIGHT ALLOWED
Height - 60'

MAXIMUM FLOOR AREA RATIO
FAR - 1.5

SETBACKS

SE Ave. - 15'
Central Ave. - 15'
Side/Rear - none

STRUCTURAL DESIGN CRITERIA :

DESIGN LOADS

Roof live loads, Lr
Total roof dead load

WIND DESIGN

Basic wind speed, Vult
Wind exposure category
Wind load importance factor, I
Internal pressure coefficient, GCpi

SEISMIC DESIGN DATA


Risk category
Site class
Seismic importance factor, I
Mapped spectral accelerations, Sa/S1
Design spectral accelerations, SDS/SD1
Seismic design category

SPECIAL INSPECTIONS :

PER CBC & S0.01

Structural steel - including welding, high-strength bolting, and anchors as noted.

VICINITY MAP

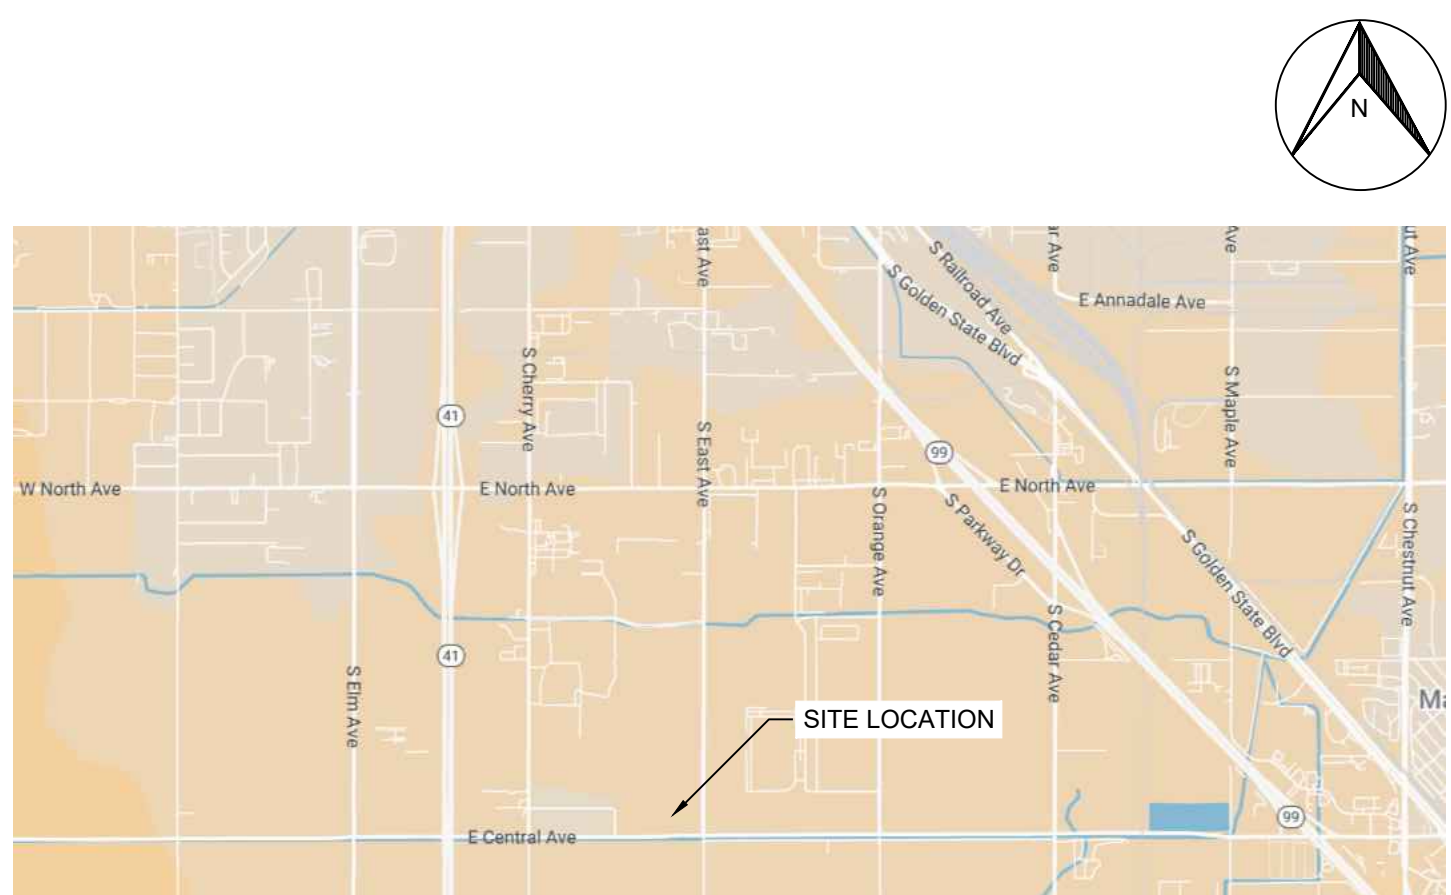


SITE PLAN



10590 ARMSTRONG AVENUE
MATHER, CALIFORNIA 95655
(916) 520-2100

THE PLANS AND SPECIFICATIONS HEREIN ARE OWNED BY AND FOR THE SOLE USE OF ACCO ENGINEERED SYSTEMS, INC. ("ACCO") THE "DESIGN BUILDER", AND MAY NOT BE REPRODUCED OR USED BY OTHERS FOR ANY PURPOSE UNLESS AUTHORIZED BY ACCO IN WRITING. ACCO CANNOT ACCEPT ANY LIABILITY, WARRANTY, OR OBLIGATION IN THE EVENT OF UNAUTHORIZED USE.

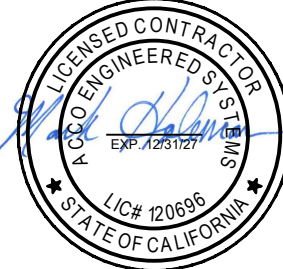

B	01-12-2026	PLAN CHECK 1	AJR
A	12-10-2025	ISSUED FOR PERMIT	AJR
No.	Date	Description	By

Revisions

Project

ULTA BEAUTY WAREHOUSE

850 EAST CENTRAL AVE
FRESNO, CA 93706

Title

TITLE SHEET

A. ROMERO

Designed By
A. ROMERO
Drawn By
70981292
Job Number

M. HOLEMAN

Checked By
K. DUNN
Project Manager
NONE
Scale

G0.00