


ULTA BEAUTY WAREHOUSE

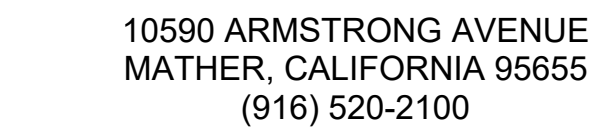

MECHANICAL SYMBOL LEGEND							
SYMBOL		DESCRIPTION		SYMBOL		DESCRIPTION	
(N)	NEW (N) & EXISTING (E) RECTANGULAR SUPPLY AIR DUCT RISER		SUPPLY AIR GRILLE		PNEUMATIC 2W-CV		FLEX CONNECTOR
(N)	NEW (N) & EXISTING (E) RECTANGULAR OUTSIDE AIR DUCT RISER		RETURN AIR GRILLE		PNEUMATIC 3W-CV		TWIN RUBBER SPHERICAL CONNECTOR
(N)	NEW (N) & EXISTING (E) RECTANGULAR RETURN AIR DUCT RISER		EXHAUST GRILLE		PNEUMATIC BUTTERFLY 2W-CV		TRIPLE GROOVED FLEXIBLE COUPLINGS - COUPLINGS MAY BE SEPARATED AS LONG AS THERE ARE THREE IN A STRAIGHT LINE BETWEEN THE ROTATING EQUIPMENT AND THE HEADER
(N)	NEW (N) & EXISTING (E) RECTANGULAR EXHAUST AIR DUCT RISER		ROUND DIFFUSER		PNEUMATIC BUTTERFLY 3W-CV (DIVERTING)		END CAP
(N)	NEW (N) & EXISTING (E) ROUND AIR DUCT RISER		LINEAR DIFFUSER		PNEUMATIC BUTTERFLY 3W-CV (MIXING)		BLIND FLANGE
	NEW SINGLE LINE & DOUBLE LINE RECTANGULAR OR ROUND DUCT		SIDE WALL GRILLE		MOTORIZED 2W-CV		CONCENTRIC REDUCER
	EXISTING SINGLE LINE & DOUBLE LINE RECTANGULAR OR ROUND DUCT		WALL LOUVER		MOTORIZED 3W-CV		ECCENTRIC REDUCER
	EXISTING SINGLE LINE DUCTWORK TO BE DEMOLISHED ("X" OPTION)		SPIRAL SIDEWALL (WITH EXTRACTOR & WITHOUT EXTRACTOR)		MOTORIZED BUTTERFLY 2W-CV		UNION
	EXISTING DOUBLE LINE DUCTWORK TO BE DEMOLISHED ("X" OPTION)		FLEXIBLE DUCT		MOTORIZED BUTTERFLY 3W-CV (DIVERTING)		SCHRADER VALVE
	EXISTING DOUBLE LINE DUCTWORK TO BE DEMOLISHED ("X" OPTION)		SECTION NUMBER SECTION CALL OUT SYMBOL SHEET NUMBER		MOTORIZED BUTTERFLY 3W-CV (MIXING)		FLOW ARROW
	DUCT WITH LINING DIMENSIONS SHOWN ARE G.D. OF SHEETMETAL (W X H) THICKNESS OF INSULATION AS SHOWN ON PLANS		GRILLE TYPE, DIFFUSER NECK SIZE AIR VOLUME CUBIC FEET PER MINUTE - AIR THROW PATTERN		GATE VALVE		PRESSURE GAUGE WITH SHUT-OFF VALVE
	SINGLE & DOUBLE LINE DUCTWORK WITH TRANSITIONAL FITTING		EQUIPMENT LABEL TAG		BALL VALVE		TEMPERATURE SENSOR & THERMOWELL
	DOUBLE LINE SQUARE TO ROUND TRANSITIONAL FITTING		FLOW ARROW & FLOW ARROW - CURVED		BALL VALVE WITH MEMORY STOP		THERMOMETER
	90° RADIUS ELBOW 90° SQUARE ELBOW WITH TURNING VANES		REVISION CLOUD		GLOBE VALVE		PET'S PLUG
	90° ROUND DUCT TURNING VERTICAL 90° RECT. DUCT TURNING VERTICAL		REVISION DELTA		BUTTERFLY VALVE		FLOW SWITCH
	SINGLE LINE MANUAL VOLUME DAMPER		ELECTRICAL EQUIPMENT CONNECTION LOCATION BY ELECTRICAL CONTRACTOR		CHECK VALVE		TRIPLE DUTY VALVE
	DOUBLE LINE MANUAL VOLUME DAMPER		GAS STUB-UP BY PLUMBING CONTRACTOR		STRAINER		RELIEF VALVE
	MOTORIZED DAMPER (ELECTRIC)		COLD WATER STUB-UP BY PLUMBING CONTRACTOR		STRAINER WITH BLOWDOWN VALVE		3-WAY WAX VALVE
	MOTORIZED DAMPER (PNEUMATIC)		CONDENSATE LINE WITH TRAP TO APPROVED RECEPTOR BY PLUMBING CONTRACTOR		BASKET STRAINER		VACUUM BREAKER
	FIRE DAMPER (SINGLE LINE AND DOUBLE LINE)		FLOOR SINK WITH TRAP TO APPROVED RECEPTOR BY PLUMBING CONTRACTOR		SUCTION DIFFUSER		STEAM TRAP
	FIRE/SMOKE DAMPER (SINGLE LINE AND DOUBLE LINE)		CEILING OR DUCT ACCESS PANEL BY GENERAL CONTRACTOR		AIR VENT - MANUAL		ANGLE VALVE
	SMOKE DETECTOR (DUCT TYPE)		POINT OF CONNECTION		AIR VENT - AUTO		SIGHT GLASS
	STATIC PRESSURE SENSOR		THERMOSTAT WITH ZONE NUMBER		PRESSURE REDUCING VALVE / GAS REGULATOR VALVE		FILTER DRIER
	SMOKE DETECTOR (AREA TYPE)		HUMIDITY SENSOR		PRESSURE SUSTAINING VALVE		SOLENOID VALVE
	CO2 SENSOR		REGULATOR		AUTO FLOW CONTROL		TXV WITH SENSING BULB
	NO2 SENSOR		WALL SWITCH		CIRCUIT SETTER		PRESSURE GAUGE - STEAM
	CO SENSOR				BALL VALVE WITH HOSE CONNECTION		HOSE BIBB
	OCCUPANCY SENSOR				FLOW METER INLINE		DIFFERENTIAL PRESSURE SENSOR ASSEMBLY BY BAS
					FLOW METER TURBINE		

DRAWING INDEX KEY											
SHEET NO		SHEET TITLE		DRAWING ISSUE	DATE	ISSUED FOR PERMIT					
						PLAN CHECK 1					
		NOT INCLUDED WITH ISSUE			12-10-2025						
		NEW OR REVISED			01-09-2026						
		NO CHANGES									
				REVISION	A	B					
M0.00	COVER SHEET, DRAWING INDEX, & SYMBOL LEGEND				•	•					
M0.01	CONSTRUCTION REQUIREMENTS				•	•					
M0.10	EQUIPMENT SCHEDULES				•	•					
M1.01A	MECHANICAL LEVEL 01				•	•					
M1.02	MECHANICAL ROOF				•	•					
M5.01	DETAILS AND DIAGRAM				•	•					
M5.02	DETAILS AND DIAGRAM (CONTINUED)				•	•					
M10.01	ENERGY CODE				•	•					
M10.02	ENERGY CODE (CONTINUED)				•	•					

[illegible]

ABBREVIATIONS					
ABBR.	DESCRIPTION	ABBR.	DESCRIPTION	ABBR.	DESCRIPTION
AFH	ABOVE FINISHED FLOOR	FLU	FLUE	OPNG	OPENING
AHJ	AUTHORITY HAVING JURISDICTION	FR	FLOOR RETURN	OSA	OUTSIDE AIR
AP	ACCESS PANEL	FS	FLOOR SUPPLY	PLBG	PLUMBING
ASD	AREA SMOKE DETECTOR	FSD	FIRE SMOKE DAMPER	POC	POINT OF CONNECTION
ABF	BACKFLOW DAMPER	GAUGE	GALVANEZ	RELOCATE	RELOCATE
BSF	BOTTOM FLAT	GALV	GALVANIZED	RA	RETURN AIR
BOP	BOTTOM OF DECK	GC	GENERAL CONTRACTOR	RECIP	RECIPROCATING
BOP	BOTTOM OF PULTRUSION	GE	GREASE EXHAUST AIR	REQD	REQUIRED
BOD	BOTTOM OF PIPE	GPH	GALLONS PER HOUR	REV	REVISION
CB	COMPRESSED AIR	GPM	GALLONS PER MINUTE	RG	RETURN OR TRANSFER RHILL
CE	CONDENSATE	GLYC	GALLON RETURN	RH	REFRIGERANT GAS (HIGH PRESSURE)
CD	CEILING EXHAUST	GLYC	GALLON SILENT	REHAT	REHEAT
CENTR	CENTRIFUGAL	GYP BO	GYPSTUM BOARD	RL	REFRIGERANT LIQUID
CF	CAP FOR FUTURE	HHWR	HEATING HOT WATER RETURN	RMF	RAPID MOUNT FRAME
CHM	CUBIC FEET PER MINUTE	HHW	HEATING HOT WATER SUPPLY	RND	ROUND NECK ADAPTER
CHWR	CHILLED WATER RETURN	HOA	HAND-OFF-AUTO	RND	ROUND
CHWS	CHILLED WATER SUPPLY	HPS	HIGH PRESSURE GAS	RR	REFRIGERANT RELIEF
CHW	CENTRIFUGAL	HPS	HIGH PRESSURE STEAM	SND	SOUND
CLM	CEILING	HT	HEIGHT	SA	SUPPLY AIR
CMG	CONCRETE MASONRY UNIT	HVLS	HIGH VOLUME LOW SPEED FAN	SG	SUPPLY GRILLE
CO	COOLING ONLY	ID	INSIDE DIMENSION	SM	SHEET METAL
COMB	COMBUSTION AIR	INS	INSULATION	STD	STAINLESS STEEL
CONC	CONCRETE	INT	INTERIOR	STD	STANDARD
CONN	CONNECTION	(L)	LINEAR	TD	TRANSFER AIR
CONTR	CONTRACTOR	LPS	LOW PRESSURE STEAM	TD	TOP DOWN
CR	STEAM CONDENSATE RETURN	LR	LEAD RETURN	TF	TOP FLAT
CR	CEILING RETURN	LS	LEAD SUPPLY	TOO	TOP OF DECK
CS	CEILING SUPPLY	LVG	LEAVING	TOP	TOP OF PIPE
CWS	CONDENSER WATER RETURN	MA	MIXED AIR	TSTAT	THERMOSTAT
CWS	CONDENSER WATER SUPPLY	MECH	MECHANICAL	TOP	TOP UPSTAIR
DIA	DIAMETER	MFR	MANUFACTURER	TPY	TPICAL
DWD	DUCT SMOKE DETECTOR	MP	MEDIUM PRESSURE GAS	UBC	UNIFORM BUILDING CODE
DWG	DRAWING	MTO	MOUNTED	UC	UNDERCUT
(E)	EXISTING	MTL	METAL	UG	UNDERGROUND
EXH	EXHAUST AIR	MAU	MAKE UP AIR	UMC	UNIFORM MECHANICAL CODE
ELB	ELBOW	MVD	MANUAL VOLUME DAMPER	UNC	UNLESS NOTED OTHERWISE
ELEC	ELECTRICAL	(N)	NEW	UTR	UP THROUGH ROOF
ENT	ENTERING	NA	NOT APPLICABLE	V	VENT
EQ	EQUIPMENT	NC	NORMALLY CLOSED	VAV	VARIABLE AIR VOLUME
EXH	EXHAUST	NG	NATURAL GAS	VDF	VARIABLE SPEED DRIVE
EXT	EXTERIOR	NT	NOT IN CONTRACT	VOL	VOLUME IN FIELD
(F)	FUTURE	NIS	NOT TO SCALE	VRF	VARIABLE REFRIGERANT FLOW/PIPE
FD	FIRE DAMPER	OBO	OPPOSED BLADE DAMPER	WMS	WIRE MESH SCREEN
FLR	FLEXIBLE	OC	ON CENTER	XFER	TRANSFER
		OD	OUTSIDE DIMENSION		

APPLICABLE CODES

CALIFORNIA MECHANICAL PROJECTS:

ALL WORK SHALL BE IN FULL ACCORDANCE WITH APPLICABLE
LOCAL, STATE, AND FEDERAL CODES, LAWS AND REGULATIONS.
ALL WORK AND MATERIALS SHALL BE IN FULL ACCORDANCE WITH,
BUT NOT LIMITED TO:

- CALIFORNIA CODE OF REGULATIONS (CCR)
 - 2022 CALIFORNIA BUILDING CODE - CCR TITLE 24 PART 2
 - 2022 CALIFORNIA ELECTRICAL CODE - CCR TITLE 24 PART 3
 - 2022 CALIFORNIA MECHANICAL CODE - CCR TITLE 24 PART 4
 - 2022 CALIFORNIA PLUMBING CODE - CCR TITLE 24 PART 5
 - 2022 CALIFORNIA ENERGY CODE - CCR TITLE 24 PART 6
 - 2022 CALIFORNIA FIRE CODE - CCR TITLE 24 PART 9
 - 2022 CALIFORNIA GREEN BUILDING STANDARDS CODE - CCR TITLE 24 PART 11

ALL WORK SHALL BE IN ACCORDANCE WITH THE FOLLOWING
ADDITIONAL GUIDELINES WHERE REQUIRED BY CODE:

- SHEET METAL AND AIR CONDITIONING CONTRACTORS NATIONAL ASSOCIATION (SMACNA)
- AMERICAN SOCIETY OF HEATING, REFRIGERATION AND AIR-CONDITIONING ENGINEERS (ASHRAE)
- AMERICAN SOCIETY OF MECHANICAL ENGINEERS (ASME)
- AMERICAN SOCIETY OF CIVIL ENGINEERS (ASCE)
- NATIONAL FIRE PROTECTION AGENCY (NFPA)
- OCCUPATIONAL SAFETY AND HEALTH ACT (OSHA)
- LOCAL UTILITY GUIDELINES AND REGULATIONS
- LOCAL AIR QUALITY MANAGEMENT DISTRICTS

SCOPE OF WORK

1. ADD PACKAGE UNITS AND DUCTWORK TO PROVIDE COOLING.
2. STARTUP, BALANCE, AND TEST NEW EQUIPMENT.

SITE PLAN

The site plan is an aerial photograph of the proposed industrial facility. The building footprint is outlined in black, with a white roof section and a blue roof section. A dashed line outlines the 'AREA OF WORK'. The site is bordered by a road to the north and a residential area to the south. A north arrow is located in the top right corner.

Project

**ULTA BEAUTY
WAREHOUSE**

**850 EAST CENTRAL AVE
FRESNO, CA 93706**

MO.00