


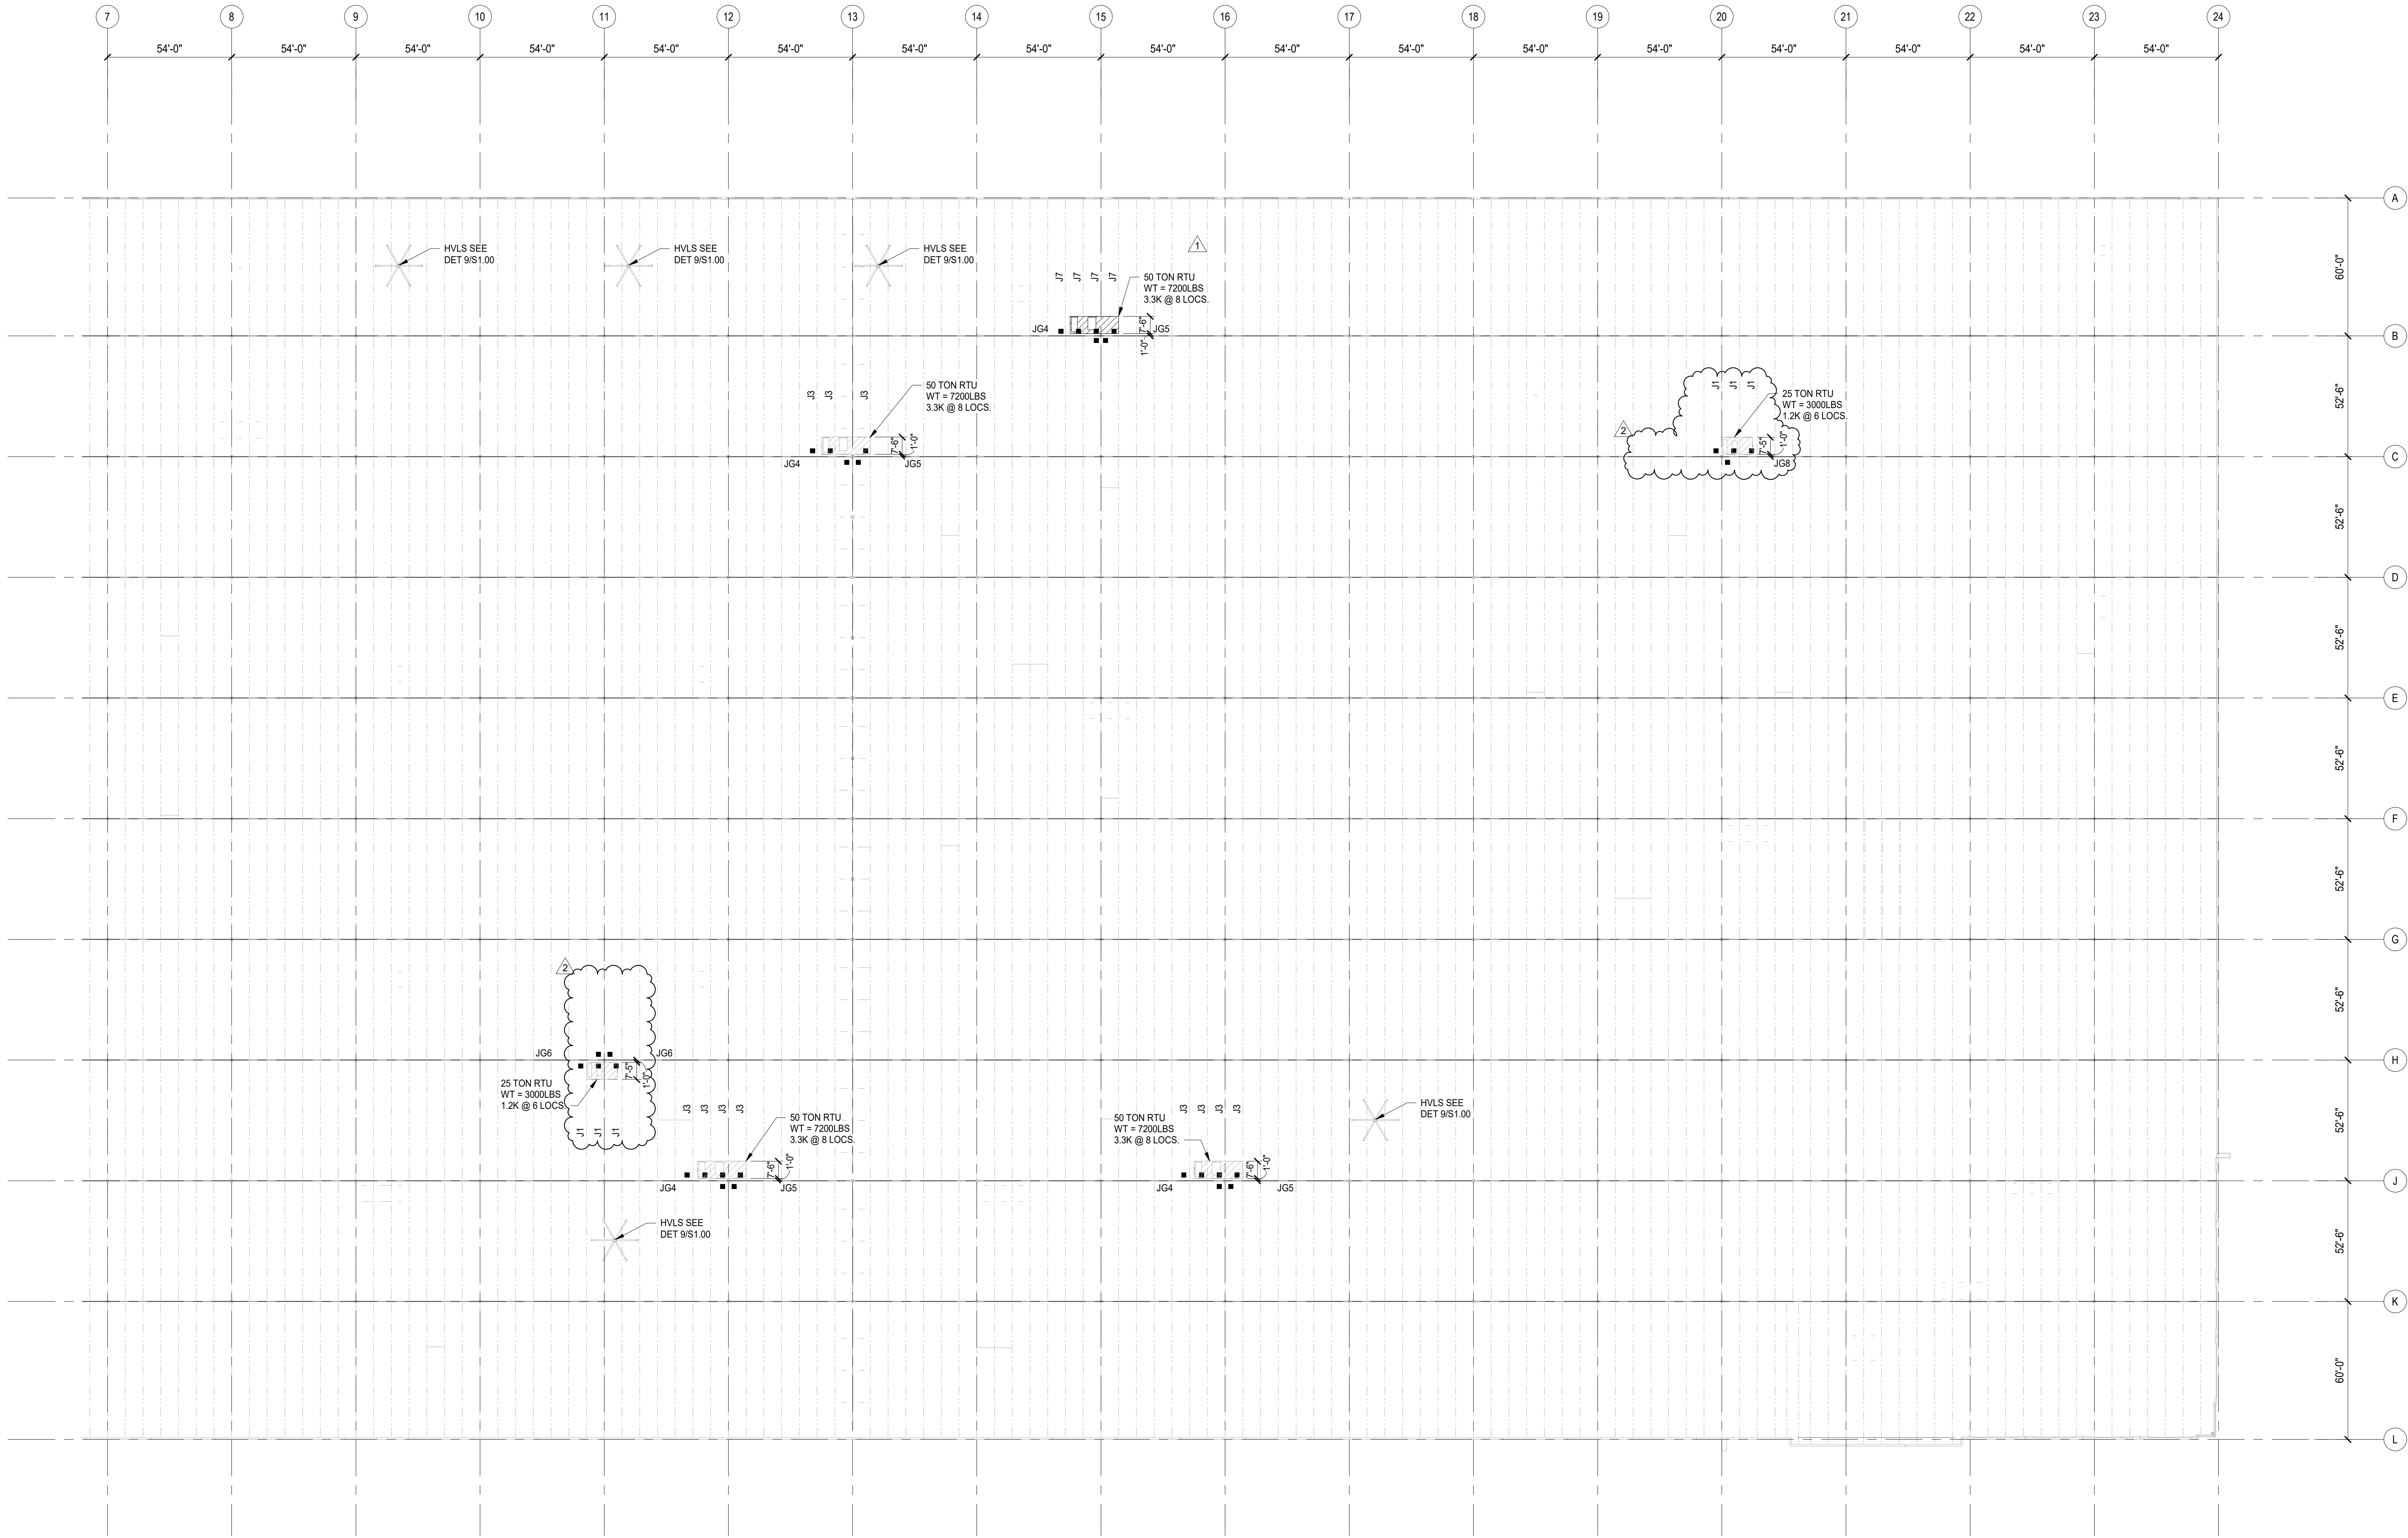

1
S2.00 1/32" = 1'-0"

EXISTING ROOF REINFORCING PLAN

- JOIST REINFORCING NOTES:
- SEE SHEET SERIES S0.XX FOR GENERAL NOTES.
 - REINFORCE THE JOISTS INDICATED ON PLAN PER DETAILS ON SHEET S1.00.
 - COORDINATE FINAL RTU LOCATIONS, SIZES, AND WEIGHTS WITH STRUCTURAL ENGINEER BEFORE FABRICATION OF ROOF MEMBERS.
 - SEE DETAIL 10/S1.00 FOR RTU FRAMING SECTIONS AND DETAILS.



REVISIONS		
No.	Description	Date
1	AC-1 RELOCATE	1/28/2026
2	AC-6 RELOCATE	2/17/2026

ALPER = AUDI
STRUCTURAL ENGINEERS

6 Cityplace Drive Suite 1025 | St. Louis, MO 63141
phone 314.432.8600 | www.alperaudi.com

ULTA BEAUTY WAREHOUSE

860 EAST CENTRAL AVE
FRESNO, CA 93706

Sheet Name:

EXISTING ROOF REINFORCING PLAN

Project Number:	25093
Date:	11/20/2025
Drawn By:	DMM
Checked By:	MCL

Sheet Number:

S2.00